


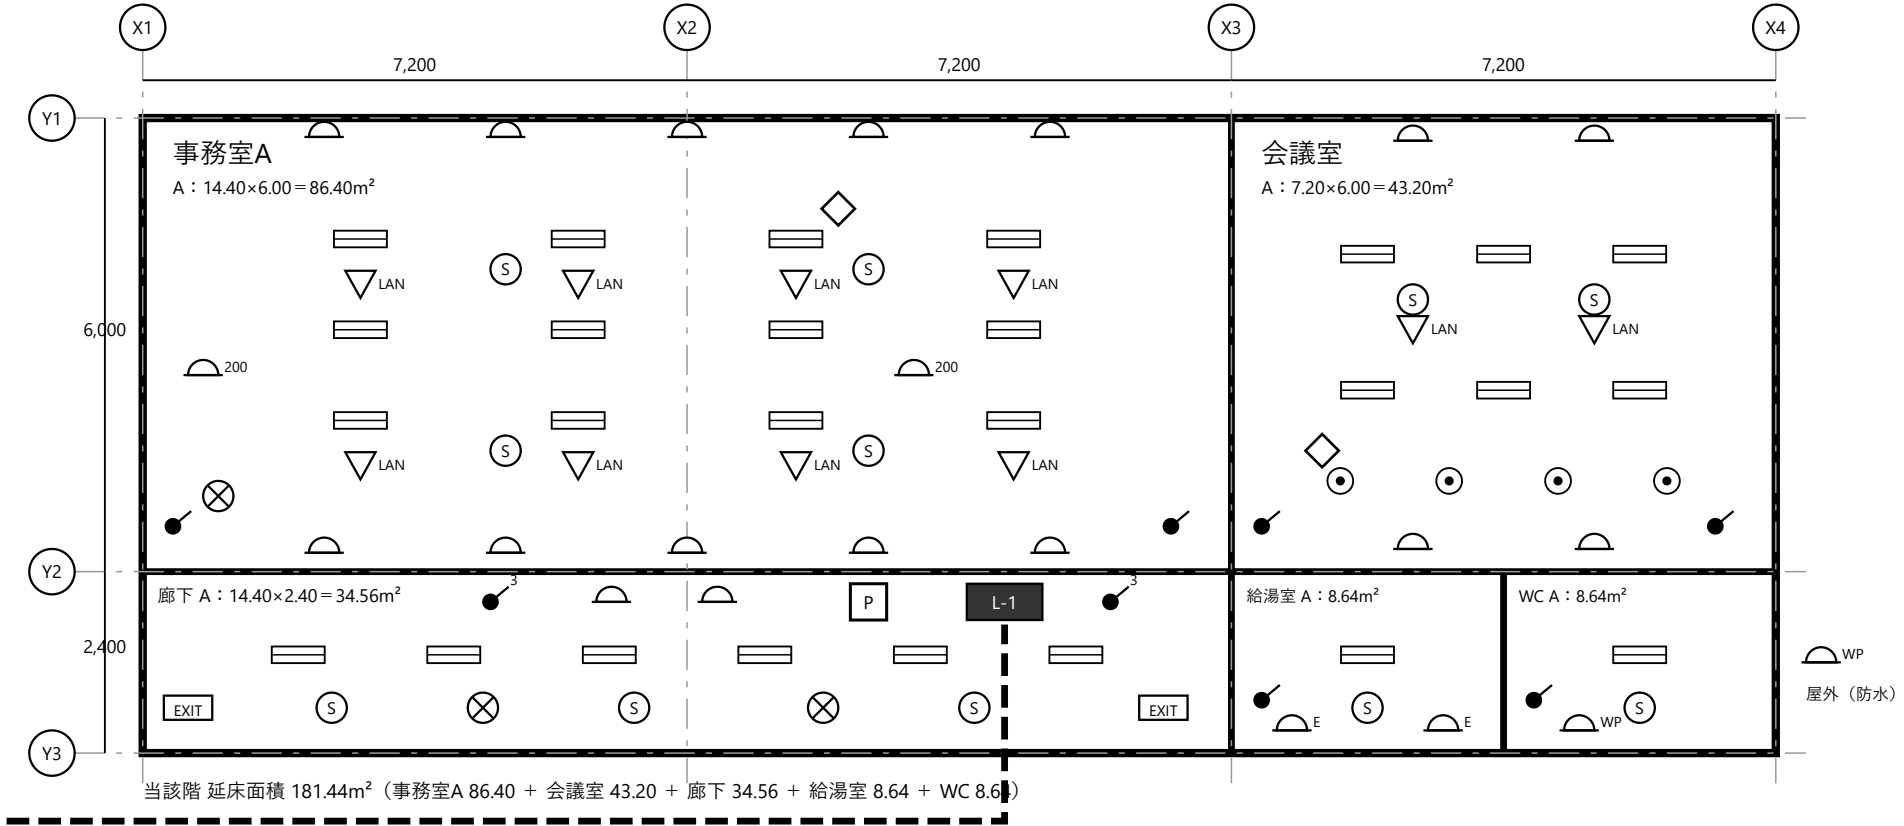

凡例（記号表）

- ベースライト 40W形2灯（LED）
- ダウンライト LED 100W形
- 非常照明（電池内蔵型）
- 誘導灯（避難口・C級）
- コンセント 一般2口 100V
- コンセント アース付
- コンセント 防水（屋外・WC）
- コンセント 200V（空調用）
- スイッチ 片切
- スイッチ 3路
- 情報コンセント（LAN CAT6）
- 煙感知器（自動火災報知設備）
- 総合盤（発信機・表示灯・地区音響）
- 分電盤 L-1（電灯分電盤）

幹線 MDF～L-1 CVT38sq×1条 平面ルート 28.5m（立上り2箇所：階高3,000）

※既設蛍光灯器具は全て撤去（18台）。撤去・処分は本工事に含む。

分電盤 L-1 回路表（主幹 ELB 3P100A）

回路	用途	器具数	電線
1	事務室A 照明	12灯	VVF1.6-2C
2	会議室 照明・ダウンライト	11灯	VVF1.6-2C
3	廊下・給湯室・WC 照明	8灯	VVF1.6-2C
4	事務室A コンセント	6	VVF2.0-2C
5	事務室A コンセント	4	VVF2.0-2C
6	会議室・廊下 コンセント	6	VVF2.0-2C
7	給湯室 アース付コンセント	2	VVF2.0-3C
8	WC・屋外 防水コンセント	2	VVF2.0-2C
9	事務室A 200V 空調	2	VVF2.0-2C
10	予備	—	—

※幹線・自火報の配線は別途（自火報は耐熱電線HPによる）

〇〇商事 事務所ビル 改修工事

1階 電気設備図（電灯・コンセント・弱電・自火報）

縮尺 S=1/100 階高 3,000 天井高 2,700

図面番号 E-01 2026年9月

※本図は拾い出し検証用に作成した架空の図面